

NAMA DESA : DESA TELUK RENDAH ILIR
NAMA POKTAN : TRI MAKMUR

PERIORITAS PERMINTAAN : 1 (SATU)
NAMA PERMINTAAN : PEMBUATAN SUMUR BOR

KEDALAMAN SUMUR : 40 M
JUMLAH : 1 TITIK

NAMA DESA : DESA TELUK RENDAH ILIR


NAMA POKTAN : TRI MAKMUR

PERIORITAS PERMINTAAN : 1 (SATU)


NAMA PERMINTAAN : PEMBANGUNAN PANEL SURYA

PANJANG PANEL : 4 m

LEBAR PANEL : 2 m

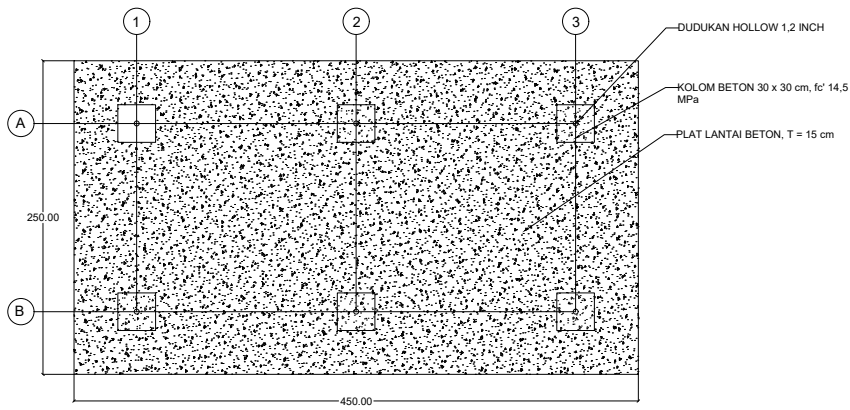

 DENAH KOLOM PANEL
SKALA 1:30

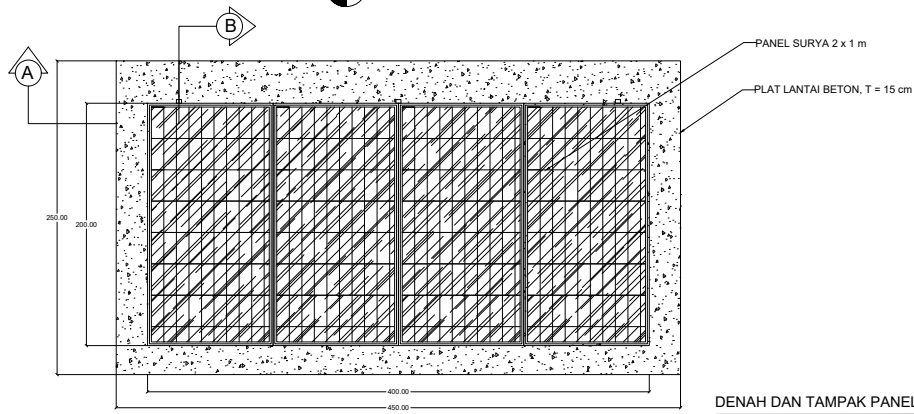

 TAMPAK ATAS PANEL
SKALA 1:30

DENAH DAN TAMPAK PANEL SURYA

Skala 1 : 30



KEMENTERIAN PERTANIAN
REPUBLIK INDONESIA
JL. HARSONO KM. NO. 3,
RAGANAN JAKARTTA 12501, INDONESIA

KETERANGAN

PRIORITAS 1

PEKERJAAN

PEMBANGUNAN PANEL SURYA

LOKASI

POKTAN TRI MAKMUR
DESA TELUK RENDAH ILIR
KEC. TEBO ILIR
KABUPATEN TEBO
PROVINSI JAMBI

DIBUAT OLEH:
UNIVERSITAS JAMBI


MUHAMMAD AMIN, S.T.
DRAFTER

DIPERIKSA :
TENAGA AHLI TEKNIK SIPIL
UNIVERSITAS JAMBI


Anna Emilawati S.T., M.Eng.
NIP. NIP. 199001222024062001

DISETUJUI :
PEJABAT PEMBUAT KOMITMEN
(PPK)

HERU SANTOSO, A.M.D., SE.
NIP. 1982031620110111007


JUDUL GAMBAR

TIPIKAL RUMAH POMPA


SATUAN

CENTIMETER

CATATAN:
SELURUH UKURAN HARUS DIPERIKSA DAN
DISEDIAKAN DILAKUKAN OLEH PELAKSANA
DAN SETIAP PERUBAHAN HARUS DIAJUKAN
KEPADA DESAHER UNTUK KLASIFIKASI SEBELUM
DILAKUKAN GAMBAR INI MENJELASKAN
MAYORITIS DESAIN.
HARUS DIPERIKSA DAN DISEDIAKAN DILAKUKAN MENUNTUT
MENDAPATKAN KEPUTUSAN DAN KEPUTUSAN DILAKUKAN
BERGASALAH ISI GAMBAR DAN DESAIN UNTUK KEPENTINGAN LAIN
TANPA DESAIN DAN DESAIN TERPILAH PERUBAHAN.

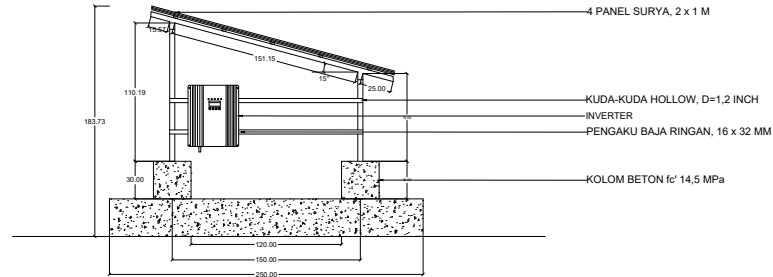

TAMPAK SAMPIING PANEL
SKALA 1:30

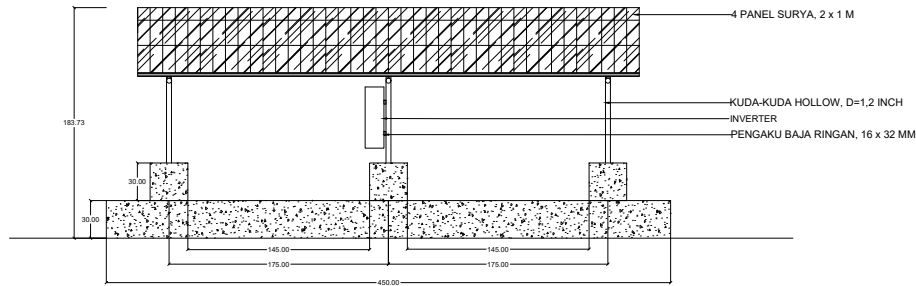

TAMPAK DEPAN PANEL
SKALA 1:30

DENAH DAN TAMPAK PANEL SURYA

Skala 1 : 30



KEMENTERIAN PERTANIAN
REPUBLIK INDONESIA

JL. HARSONO KM. NO. 3,
RAGANAN JAKARTA 12501, INDONESIA

KETERANGAN

PRIORITAS 1

PEKERJAAN

PEMBANGUNAN PANEL SURYA

LOKASI

POKTAN TRI MAKMUR
DESA TELUK RENDAH ILIR
KEC. TEBU ILIR
KABUPATEN TEBU
PROVINSI JAMBI

DIBUAT OLEH:
UNIVERSITAS JAMBI

Muhammad Amin, S.T.
MUHAMMAD AMIN, S.T.
DRAFTER

DIPERIKSA :
TENAGA AHLI TEKNIK SIPIL
UNIVERSITAS JAMBI

Anna Emiliawati S.T., M.Eng.
Anna Emiliawati S.T., M.Eng.
NIP. 199001222024062001

DISETUJUI :
PEJABAT PEMBUAT KOMITMEN
(PPK)

HERU SANTOSO, A.M.D., SE.
NIP. 1982031620110111007

JUDUL GAMBAR


TIPKAL RUMAH POMPA

SATUAN

CENTIMETER

CATATAN:

SELURUH UKURAN HARUS DIPERIKSA DAN
DIBERIKAN OLEH PELAKSANA
DAN SETIAP PERBEDAAN HARUS DIAJUKAN
KEPADA DESAINER UNTUK KLASIFIKASI SEBELUM
DIKONSTRUKSI. GAMBAR INI MENJELASKAN
MATERI DESAIN.
HARUS DIPERIKSA DAN DIBERIKAN OLEH PELAKSANA
DAN SETIAP PERBEDAAN HARUS DIAJUKAN
KEPADA DESAINER UNTUK KLASIFIKASI SEBELUM
DIKONSTRUKSI. GAMBAR INI MENJELASKAN
MATERI DESAIN.

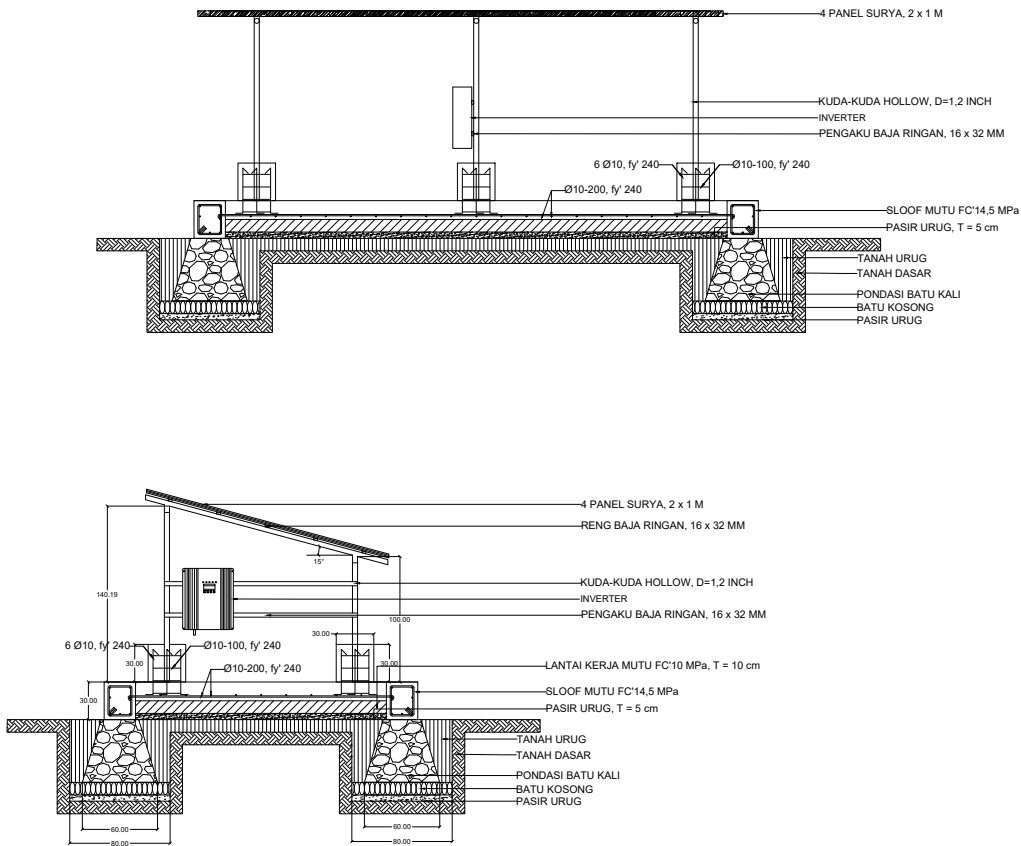

DETAIL PONDASI PANEL SURYA

Skala 1 : 30



KEMENTERIAN PERTANIAN
REPUBLIK INDONESIA

JL. HARSONO KM. NO.3,
RAGANAN JAKARTA 12501, INDONESIA

KETERANGAN

PRIORITAS 1

PEKERJAAN

PEMBANGUNAN PANEL SURYA

LOKASI

POKTAN TRI MAKMUR
DESA TELUK RENDAH ILIR
KEC. TEBU ILIR
KABUPATEN TEBU
PROVINSI JAMBI

DIBUAT OLEH:
UNIVERSITAS JAMBI

Muhammad Amin, S.T.
MUHAMMAD AMIN, S.T.
DRAFTER

DIPERIKSA :
TENAGA AHLI TEKNIK SIPIL
UNIVERSITAS JAMBI

Anna Emiliawati S.T., M.Eng.
Anna Emiliawati S.T., M.Eng.
NIP. 199001222024062001

DISETUJUI :
PEJABAT PEMBUAT KOMITMEN
(PPK)

HERU SANTOSO, A.M.D., SE.
NIP. 1982031620110111007

JUDUL GAMBAR


TIPKAL RUMAH POMPA

SATUAN

CENTIMETER

CATATAN:

SELURUH UKURAN HARUS DIPERIKSA DAN
DIBERIKAN DILAKUKAN OLEH PELAKSANA
DAN SETIAP PERBEDAAN HARUS DILAKUKAN
KEPADA DESAINER UNTUK KLASIFIKASI SEBELUM
DILAKUKAN GAMBAR INI MENJELASKAN
MAMBUK DESAIN.
HAK CPTA DILINDUNG UNDANG-UNDANG DILAKUKAN MENJELUK
MENYERUP, MENYERUPAYAKAN DAN MENYERUPAYAKAN
SEBAGAINYA ISI GAMBAR DAN DESAIN UNTUK KEPENTINGAN LAIN
TANPA IZIN DAN SEBESAR PERBEDAAN.

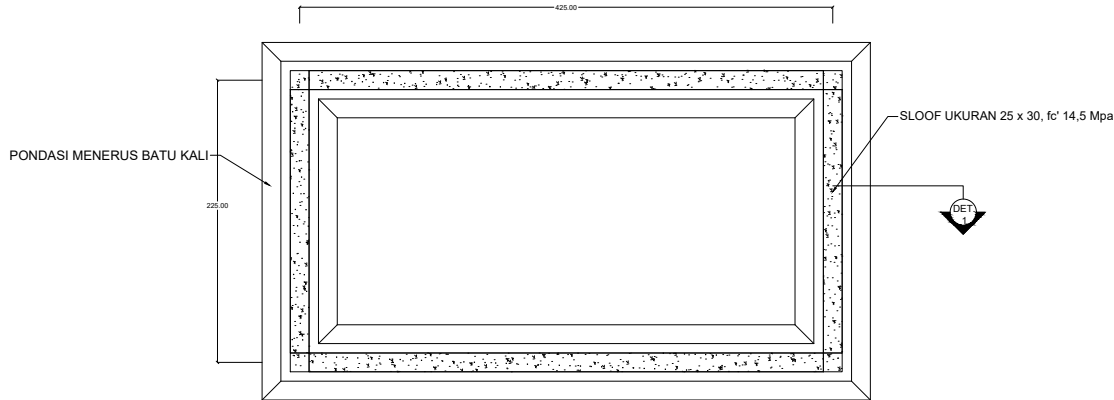

DENAH SLOOF DAN PONDASI

SKALA 1:100



KEMENTERIAN PERTANIAN
REPUBLIK INDONESIA

JL. HARSONO KM. NO. 3,
RAGANAN JAKARTA 12501, INDONESIA

KETERANGAN

PRIORITAS 1

PEKERJAAN

PEMBANGUNAN PANEL SURYA

LOKASI

POKTAN TRI MAKHMUR
DESA TELUK RENDAH ILIR
KEC. TEBO ILIR
KABUPATEN TEBO
PROVINSI JAMBI

DIBUAT OLEH :
UNIVERSITAS JAMBI

Muhammad Amin
MUHAMMAD AMIN, S.T.
DRAFTER

DIPERIKSA :
TENAGA AHLI TEKNIK SIPIL
UNIVERSITAS JAMBI

Anna Emiliawati S.T., M.Eng.
Anna Emiliawati S.T., M.Eng.
NIP. 199001222024062001

DISETUJUI :
PEJABAT PEMBUAT KOMITMEN
(PPK)


HERU SANTOSO, A.M.D., SE.
NIP. 198203162011011007

JUDUL GAMBAR

TIPIKAL RUMAH POMPA

SATUAN
CENTIMETER

CATATAN:
SELURUH UKURAN HARUS DIPERIKSA DAN
DIPERIKSA OLEH PELAKSANA
DAN SETIAP PERBEDAAN HARUS DIAJUKAN
KEPADA DESAINER UNTUK KLARIFIKASI SEBELUM
DILAKUKAN GAMBAR INI MENJELASKAN
MAYORITIS DESAIN.
HAK Cipta Dilindungi Undang-Undang. Dilarang Menjual,
Menyebarkan, Menyerahkan atau Menyalin Seluruh atau Sebagian
dari Gambar dan Desain untuk Kepentingan Lain
Tanpa Izin dan Bertanggung Jawab Perancang.

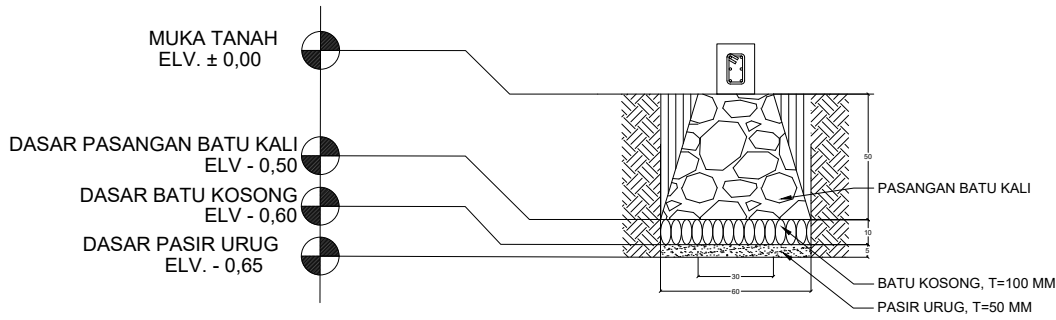

DETAIL 1 PONDASI
SKALA 1:100

	KOLOM	
	b	h
	300 x 300	
Tulangan pokok	Ø10	
Tulangan samping	Ø10 - 150	
Setinggi beton	40 mm	

	SLOOF			
	Tumpuan		Lapangan	
				
	b	h	b	h
	200 x 300		200 x 300	
Tulangan atas	2 D10		3 D10	
Tulangan bawah	3 D10		2 D10	
Tulangan samping	Ø10 - 150		Ø10 - 150	
Tulangan samping	2 D10		2 D10	
Setinggi beton	30 mm			



KEMENTERIAN PERTANIAN
REPUBLIK INDONESIA

JL. HARSONO KM. NO. 3,
RAGANAN JAKARTA 12500, INDONESIA

KETERANGAN

PRIORITAS 1

PEKERJAAN

PEMBANGUNAN PANEL SURYA

LOKASI

POKTAN TRI MAKMUR
DESA TELUK RENDAH ILIR
KEC. TEBO ILIR
KABUPATEN TEBO
PROVINSI JAMBI

DIBUAT OLEH :
UNIVERSITAS JAMBI


MUHAMMAD AMIN, S.T.
DRAFTER

DIPERIKSA :

TENAGA AHLI TEKNIK SIPIL
UNIVERSITAS JAMBI


Anna Emiliawati S.T., M.Eng.
NIP. 199001222024062001

DISETUJUI :

PEJABAT PEMBUAT KOMITMEN
(PPK)

HERU SANTOSO, A.M.D., SE.
NIP. 198203162011011007

JUJUL GAMBAR

TIPKAL RUMAH POMPA

SATUAN

CENTIMETER

CATATAN:

SELURUH UKURAN HARUS DIPERIKSA DAN
DISEKUSI OLEH PELAKSANA DAN SETIAP PERBEDAN HARUS DIAJUKAN
KEPADA DESAINER UNTUK KLAJUKAS SEBELUM
DILAKUKAN GAMBAR INI MENJELASKAN
MAYOR DESAIN.

REK CPTA DILANDUNG UNDAK-UNDANG DILANDUNG MENUTIL
RENTENKUPIL, REKUTERKUPIL DAN REKUTERKUPIL ATAS
BERAGALAN IS GAMBAR DAN DESAIN UNTUK KEPENTINGAN LAIN
TANPA DESAIN DAN DESAIN TERKUPIL PERSEKUTUAN.